


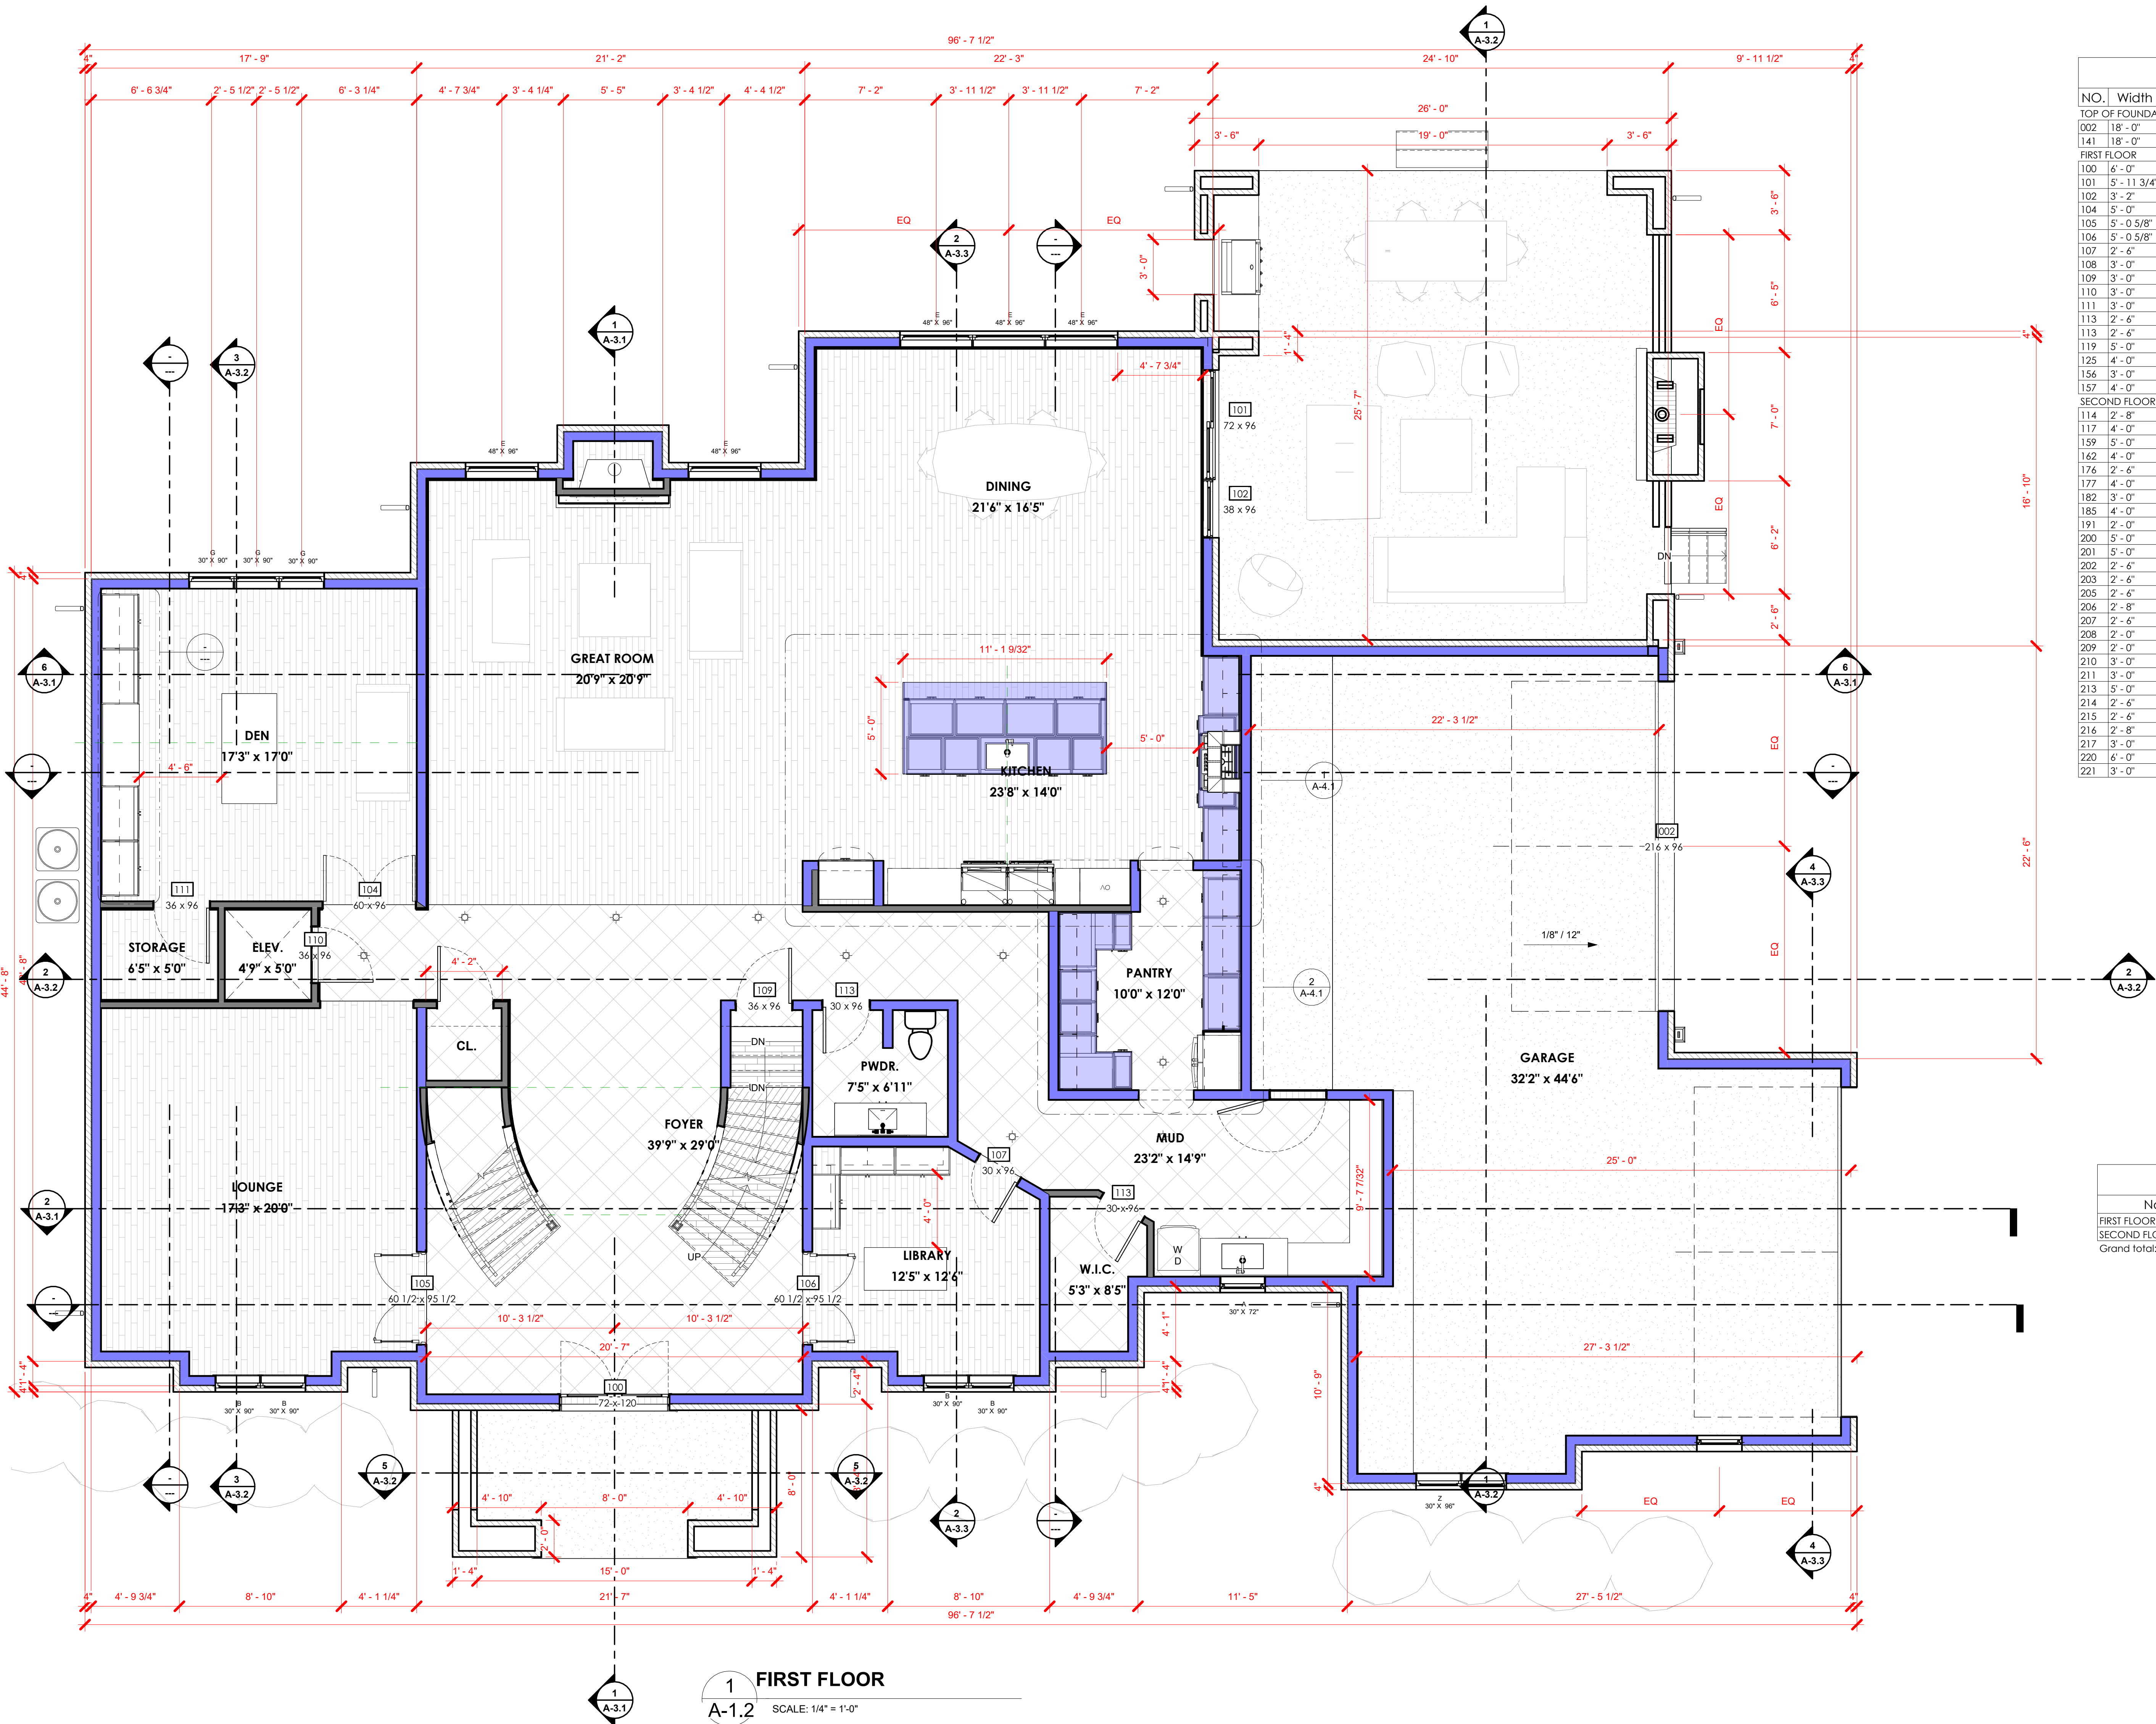

DOOR SCHEDULE				
NO.	Width	Height	Type	Comments
TOP OF FOUNDATION				
002	18' - 0"	8' - 0"	18'-0" x 8'-0"	
141	18' - 0"	8' - 0"	18'-0" x 8'-0"	
FIRST FLOOR				
100	6' - 0"	10' - 0"	HPI 60120	
101	5' - 11 3/4"	8' - 0"	5' 11-3/4" x 8' 0"	
102	3' - 2"	8' - 0"	3' 2" x 8' 0"	
104	5' - 0"	8' - 0"	Door-Double-Swing	
105	5' - 0 5/8"	7' - 11 1/2"	CUIAF5080	
106	5' - 0 5/8"	7' - 11 1/2"	CUIAF5080	
107	2' - 6"	8' - 0"	Door-Single-Swing	
108	3' - 0"	8' - 0"	Door-Single-Swing	
109	3' - 0"	8' - 0"	Door-Single-Swing	
110	3' - 0"	8' - 0"	Door-Single-Swing	
111	3' - 0"	8' - 0"	Door-Single-Swing	
113	2' - 6"	8' - 0"	Door-Single-Swing	
113	2' - 6"	8' - 0"	Door-Single-Swing	
119	5' - 0"	8' - 0"	Door-Double-Swing	
125	4' - 0"	7' - 0"	Frame-001	
156	3' - 0"	8' - 0"	Door-Single-Swing	
157	4' - 0"	7' - 0"	Frame-001	
SECOND FLOOR				
114	2' - 8"	8' - 0"	Door-Single-Swing	
117	4' - 0"	7' - 0"	Frame-001	
159	5' - 0"	8' - 0"	Door-Double-Swing	
162	4' - 0"	7' - 0"	Frame-001	
176	2' - 6"	8' - 0"	Door-Single-Swing	
177	4' - 0"	7' - 0"	Frame-001	
182	3' - 0"	8' - 0"	Door-Single-Swing	
185	4' - 0"	7' - 0"	Frame-001	
191	2' - 0"	8' - 0"	24"	
200	5' - 0"	8' - 0"	Door-Double-Swing	
201	5' - 0"	8' - 0"	Door-Double-Swing	
202	2' - 6"	8' - 0"	Door-Single-Swing	
203	2' - 6"	8' - 0"	Door-Single-Swing	
205	2' - 6"	8' - 0"	Door-Single-Swing	
206	2' - 8"	8' - 0"	Door-Single-Swing	
207	2' - 6"	8' - 0"	Door-Single-Swing	
208	2' - 0"	8' - 0"	Door-Single-Swing	
209	2' - 0"	8' - 0"	Door-Single-Swing	
210	3' - 0"	8' - 0"	Door-Single-Swing	
211	3' - 0"	8' - 0"	Door-Single-Swing	
213	5' - 0"	8' - 0"	Door-Double-Swing	
214	2' - 6"	8' - 0"	Door-Single-Swing	
215	2' - 6"	8' - 0"	Door-Single-Swing	
216	2' - 8"	8' - 0"	Door-Single-Swing	
217	3' - 0"	8' - 0"	Door-Single-Swing	
220	6' - 0"	8' - 0"	Door-Single-Swing	
221	3' - 0"	8' - 0"	Door-Single-Swing	

Area	
Name	Area
FIRST FLOOR	3345 SF
SECOND FLOOR	3003 SF
Grand total: 2	6348 SF



6523 TAMARACK DR.
TROY, MI 48068
248-854-0545
DALLEWDESIGN@GMAIL.COM
WWW.DALLEWDESIGN.ILLC.COM

REVISIONS

NO.	DATE	DESCRIPTION
1	06/05/26	DESIGN 2
2	06/18/26	PRELIM. PRICE

PROJECT NAME

PATEL RESIDENCE
13515 APPLE CREST CT.
PLYMOUTH TOWNSHIP, MI
48170

SHEET TITLE


FIRST FLOOR PLAN

SHEET DATA

SCALE: 1/4" = 1'-0"
JOB:
ISSUE DATE: 07/08/26

SHEET NUMBER

A-1.2

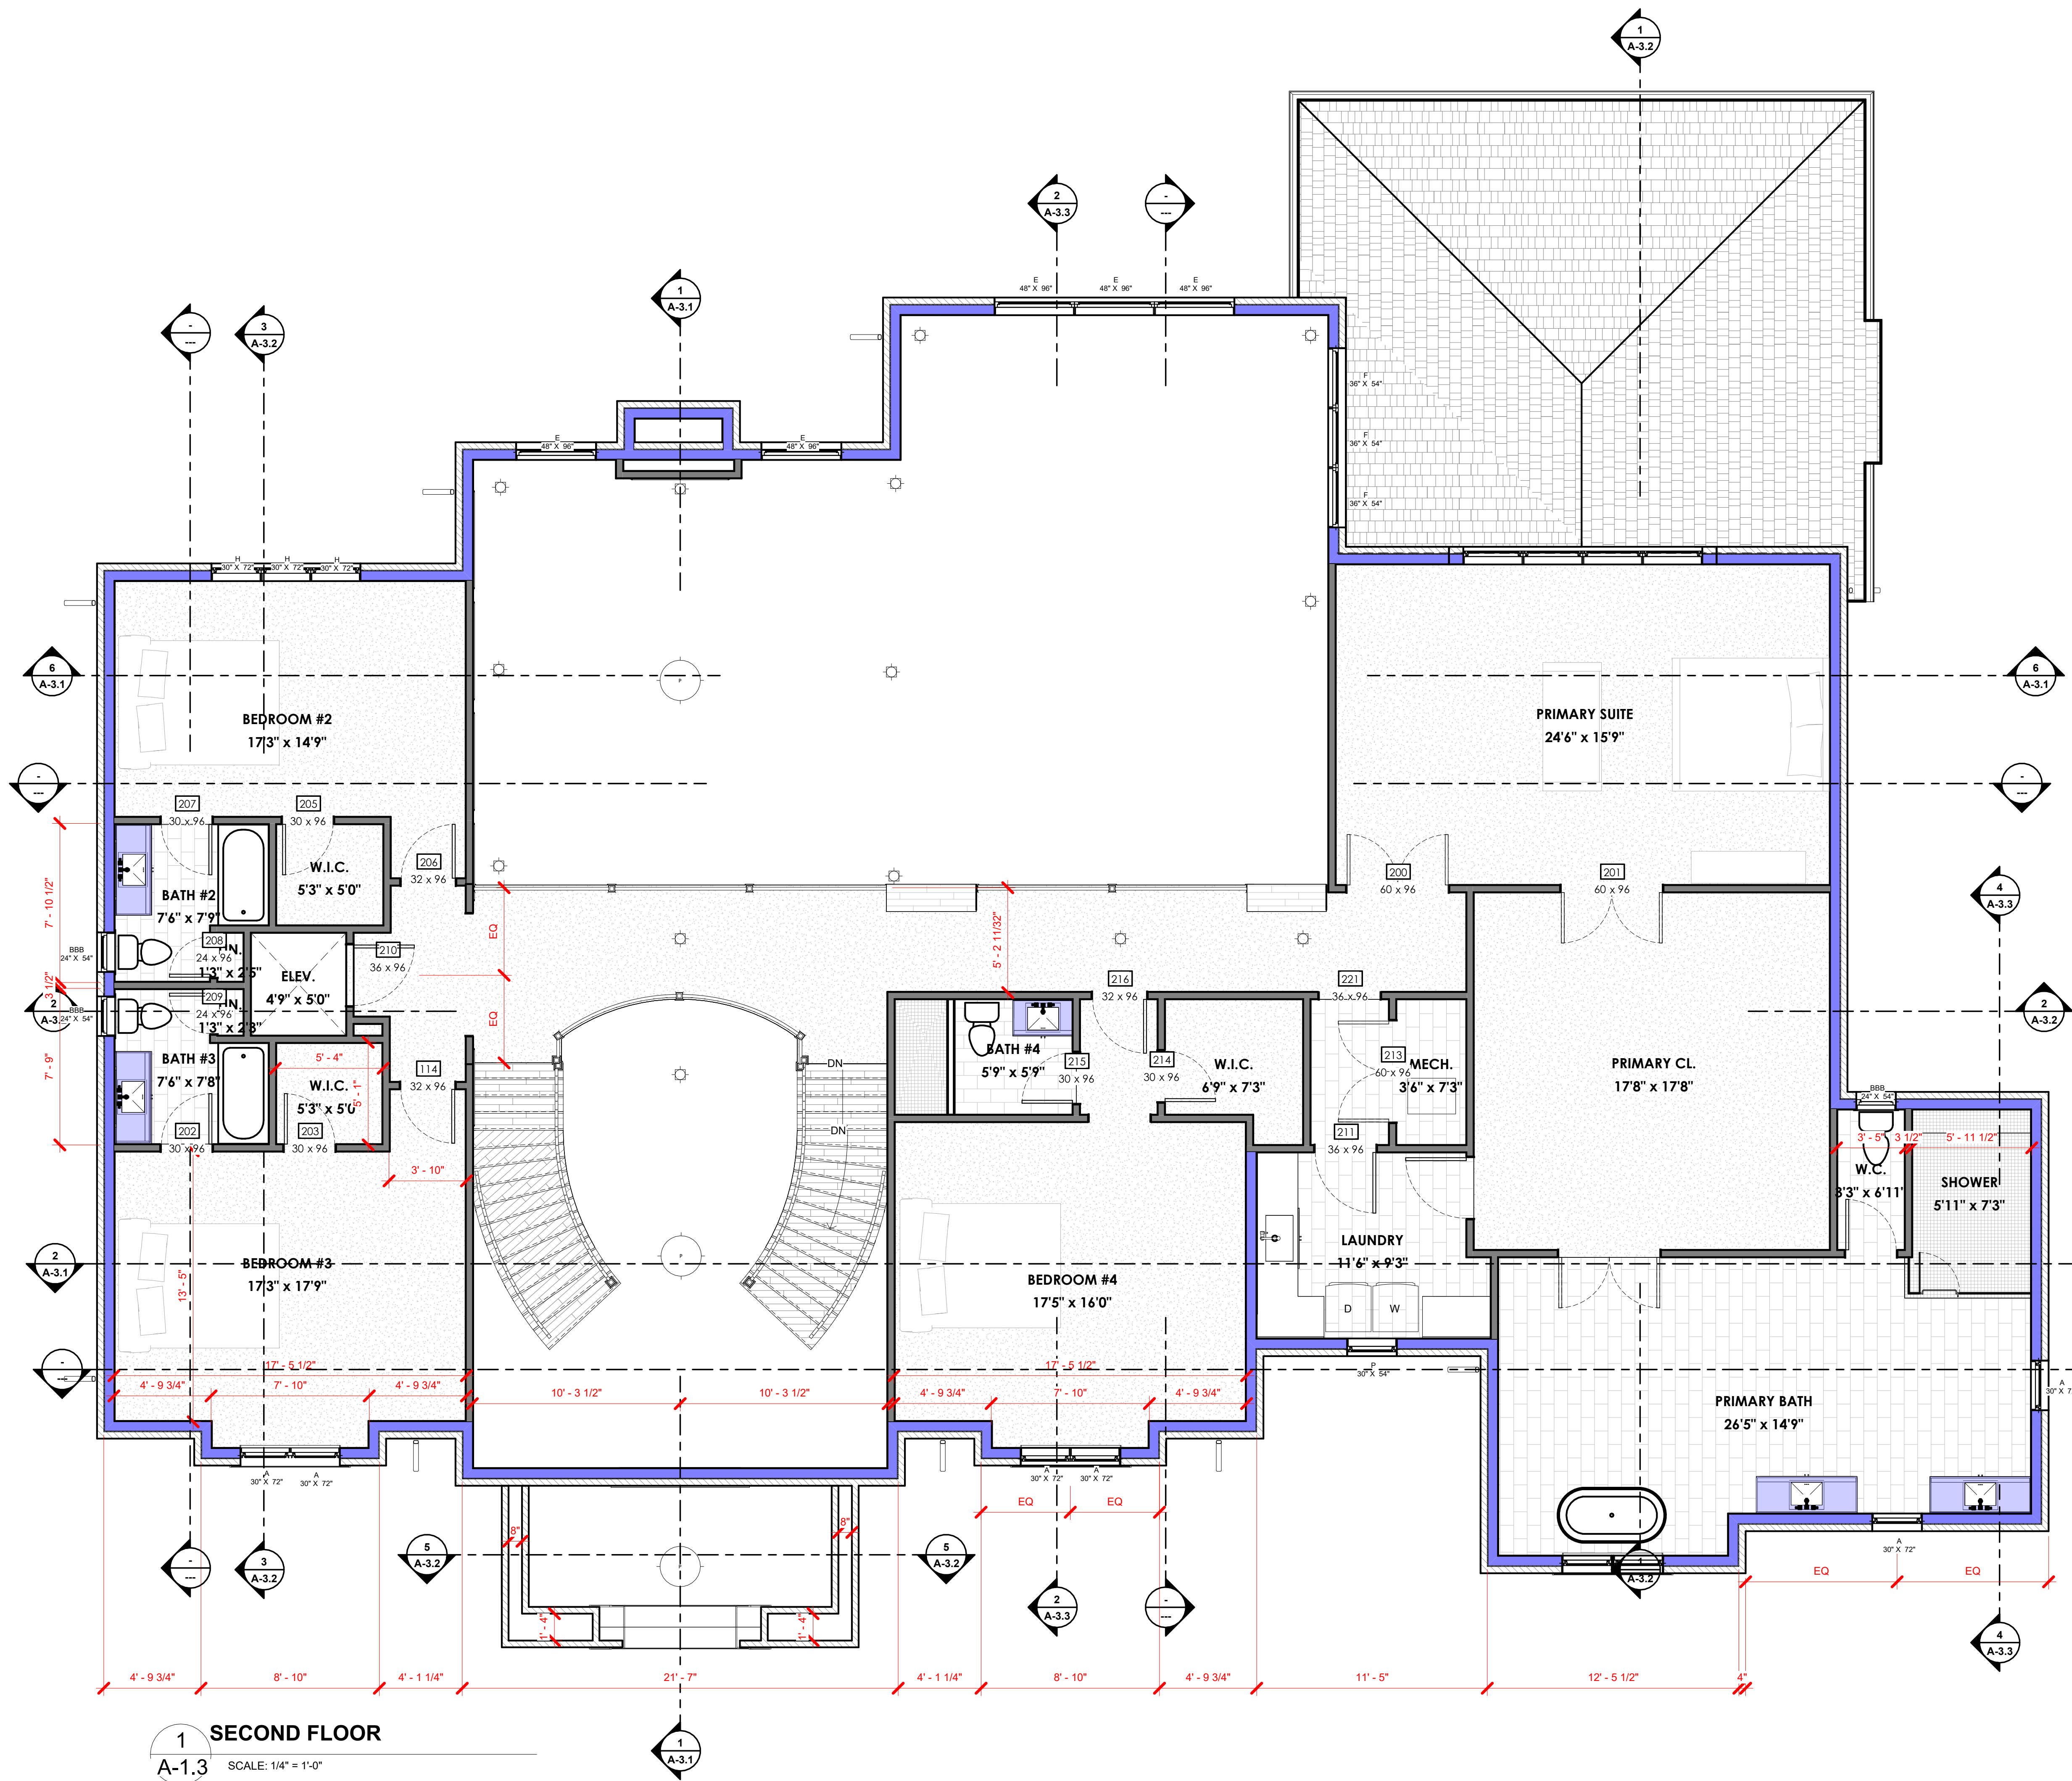

DOOR SCHEDULE				
NO.	Width	Height	Type	Comments
TOP OF FOUNDATION				
002	18'-0"	8'-0"	18'-0" x 8'-0"	
141	18'-0"	8'-0"	18'-0" x 8'-0"	
FIRST FLOOR				
100	6'-0"	10'-0"	HPI 60120	
101	5'-11 3/4"	8'-0"	5'-11 3/4" x 8'-0"	
102	3'-2"	8'-0"	3'-2" x 8'-0"	
104	5'-0"	8'-0"	Door-Double-Swing	
105	5'-0 5/8"	7'-11 1/2"	CUIAF5080	
106	5'-0 5/8"	7'-11 1/2"	CUIAF5080	
107	2'-6"	8'-0"	Door-Single-Swing	
108	3'-0"	8'-0"	Door-Single-Swing	
109	3'-0"	8'-0"	Door-Single-Swing	
110	3'-0"	8'-0"	Door-Single-Swing	
111	3'-0"	8'-0"	Door-Single-Swing	
113	2'-6"	8'-0"	Door-Single-Swing	
113	2'-6"	8'-0"	Door-Single-Swing	
119	5'-0"	8'-0"	Door-Double-Swing	
125	4'-0"	7'-0"	Frame-001	
156	3'-0"	8'-0"	Door-Single-Swing	
157	4'-0"	7'-0"	Frame-001	
SECOND FLOOR				
114	2'-8"	8'-0"	Door-Single-Swing	
117	4'-0"	7'-0"	Frame-001	
159	5'-0"	8'-0"	Door-Double-Swing	
162	4'-0"	7'-0"	Frame-001	
176	2'-6"	8'-0"	Door-Single-Swing	
177	4'-0"	7'-0"	Frame-001	
182	3'-0"	8'-0"	Door-Single-Swing	
185	4'-0"	7'-0"	Frame-001	
191	2'-0"	8'-0"	24"	
200	5'-0"	8'-0"	Door-Double-Swing	
201	5'-0"	8'-0"	Door-Double-Swing	
202	2'-6"	8'-0"	Door-Single-Swing	
203	2'-6"	8'-0"	Door-Single-Swing	
205	2'-6"	8'-0"	Door-Single-Swing	
206	2'-8"	8'-0"	Door-Single-Swing	
207	2'-6"	8'-0"	Door-Single-Swing	
208	2'-0"	8'-0"	Door-Single-Swing	
209	2'-0"	8'-0"	Door-Single-Swing	
210	3'-0"	8'-0"	Door-Single-Swing	
211	3'-0"	8'-0"	Door-Single-Swing	
213	5'-0"	8'-0"	Door-Double-Swing	
214	2'-6"	8'-0"	Door-Single-Swing	
215	2'-6"	8'-0"	Door-Single-Swing	
216	2'-8"	8'-0"	Door-Single-Swing	
217	3'-0"	8'-0"	Door-Single-Swing	
220	6'-0"	8'-0"	Door-Single-Swing	
221	3'-0"	8'-0"	Door-Single-Swing	



6523 TAMMARA CK.
TROY, MI 48098
248-854-0545
BALLEWDESIGN@GMAIL.COM
WWW.BALLEWDESIGN.ILL.COM

REVISIONS

NO.	DATE	DESCRIPTION
1	06/05/26	DESIGN 2
2	06/18/26	PRELIM. PRICE

PROJECT NAME

PATEL RESIDENCE
13515 APPLE CREST CT.
PLYMOUTH TOWNSHIP, MI
48170

SHEET TITLE

SECOND FLOOR PLAN

SHEET DATA

SCALE: 1/4" = 1'-0"
JOB:
ISSUE DATE: 07/08/26

SHEET NUMBER

A-1.3

Window Schedule				
Mark	Type	Width	Height	Count
A	29'-1/2" x 71'-1/2"	2' - 5 1/2"	5' - 11 1/2"	10
B	29'-1/2" x 89'-1/2"	2' - 5 1/2"	7' - 5 1/2"	4
BBB	23'-1/2" x 53'-1/2"	1' - 11 1/2"	4' - 5 1/2"	3
E	47'-1/2" x 95'-1/2"	3' - 11 1/2"	7' - 11 1/2"	10
F	35'-1/2" x 53'-1/2"	2' - 11 1/2"	4' - 5 1/2"	3
G	29'-1/2" x 89'-1/2" NO DL	2' - 5 1/2"	7' - 5 1/2"	3
H	29'-1/2" x 71'-1/2"	2' - 5 1/2"	5' - 11 1/2"	3
M	24" Diameter	2' - 0"		2
P	29'-1/2" x 53'-1/2"	2' - 5 1/2"	4' - 5 1/2"	1
R	Custom2.2	4' - 11 3/4"	4' - 1"	3
T	Custom4	5' - 11 3/4"	6' - 1"	1
Y	Basement_Egress_Window_Well_154' - 0"	4' - 0"		1
YYYYY	35'-1/2" x 59'-1/2"	2' - 11 1/2"	4' - 11 1/2"	4
Z	29'-1/2" x 95'-1/2"	2' - 5 1/2"	7' - 11 1/2"	2
				50

EXTERIOR FINISHES		
Material: Mark	Material: Description	Material: Area
G-1	1X6 FASCIA,RAKE AND WINDOW TRIM	1266 SF
M-1	VENEER BRICK	8866 SF
M-2	LIMESTONE	683 SF
R-1	ASPHALT SHINGLE	7956 SF
R-2	STANDING SEAM METAL ROOFING	55 SF
R-3	POWDER COATED DECORATIVE ROOF SPIRE	4 SF
S-1	1X6 FASCIA,RAKE AND WINDOW TRIM	1068 SF



6523 TAMMARA CK DR.
TROY, MI 48098
248-854-0545
DALLEWDESIGN@GMAIL.COM
WWW.DALLEWDESIGNSLLC.COM

REVISIONS

NO.	DATE	DESCRIPTION
1	06/05/26	DESIGN 2
2	06/18/26	PRELIM. PRICE

PROJECT NAME

PATEL RESIDENCE
13515 APPLE CREST CT.
PLYMOUTH TOWNSHIP, MI
48170

SHEET TITLE

ELEVATIONS

SHEET DATA


SCALE: 1/4" = 1'-0"

JOB:

ISSUE DATE: 07/08/26

SHEET NUMBER


A-2.1

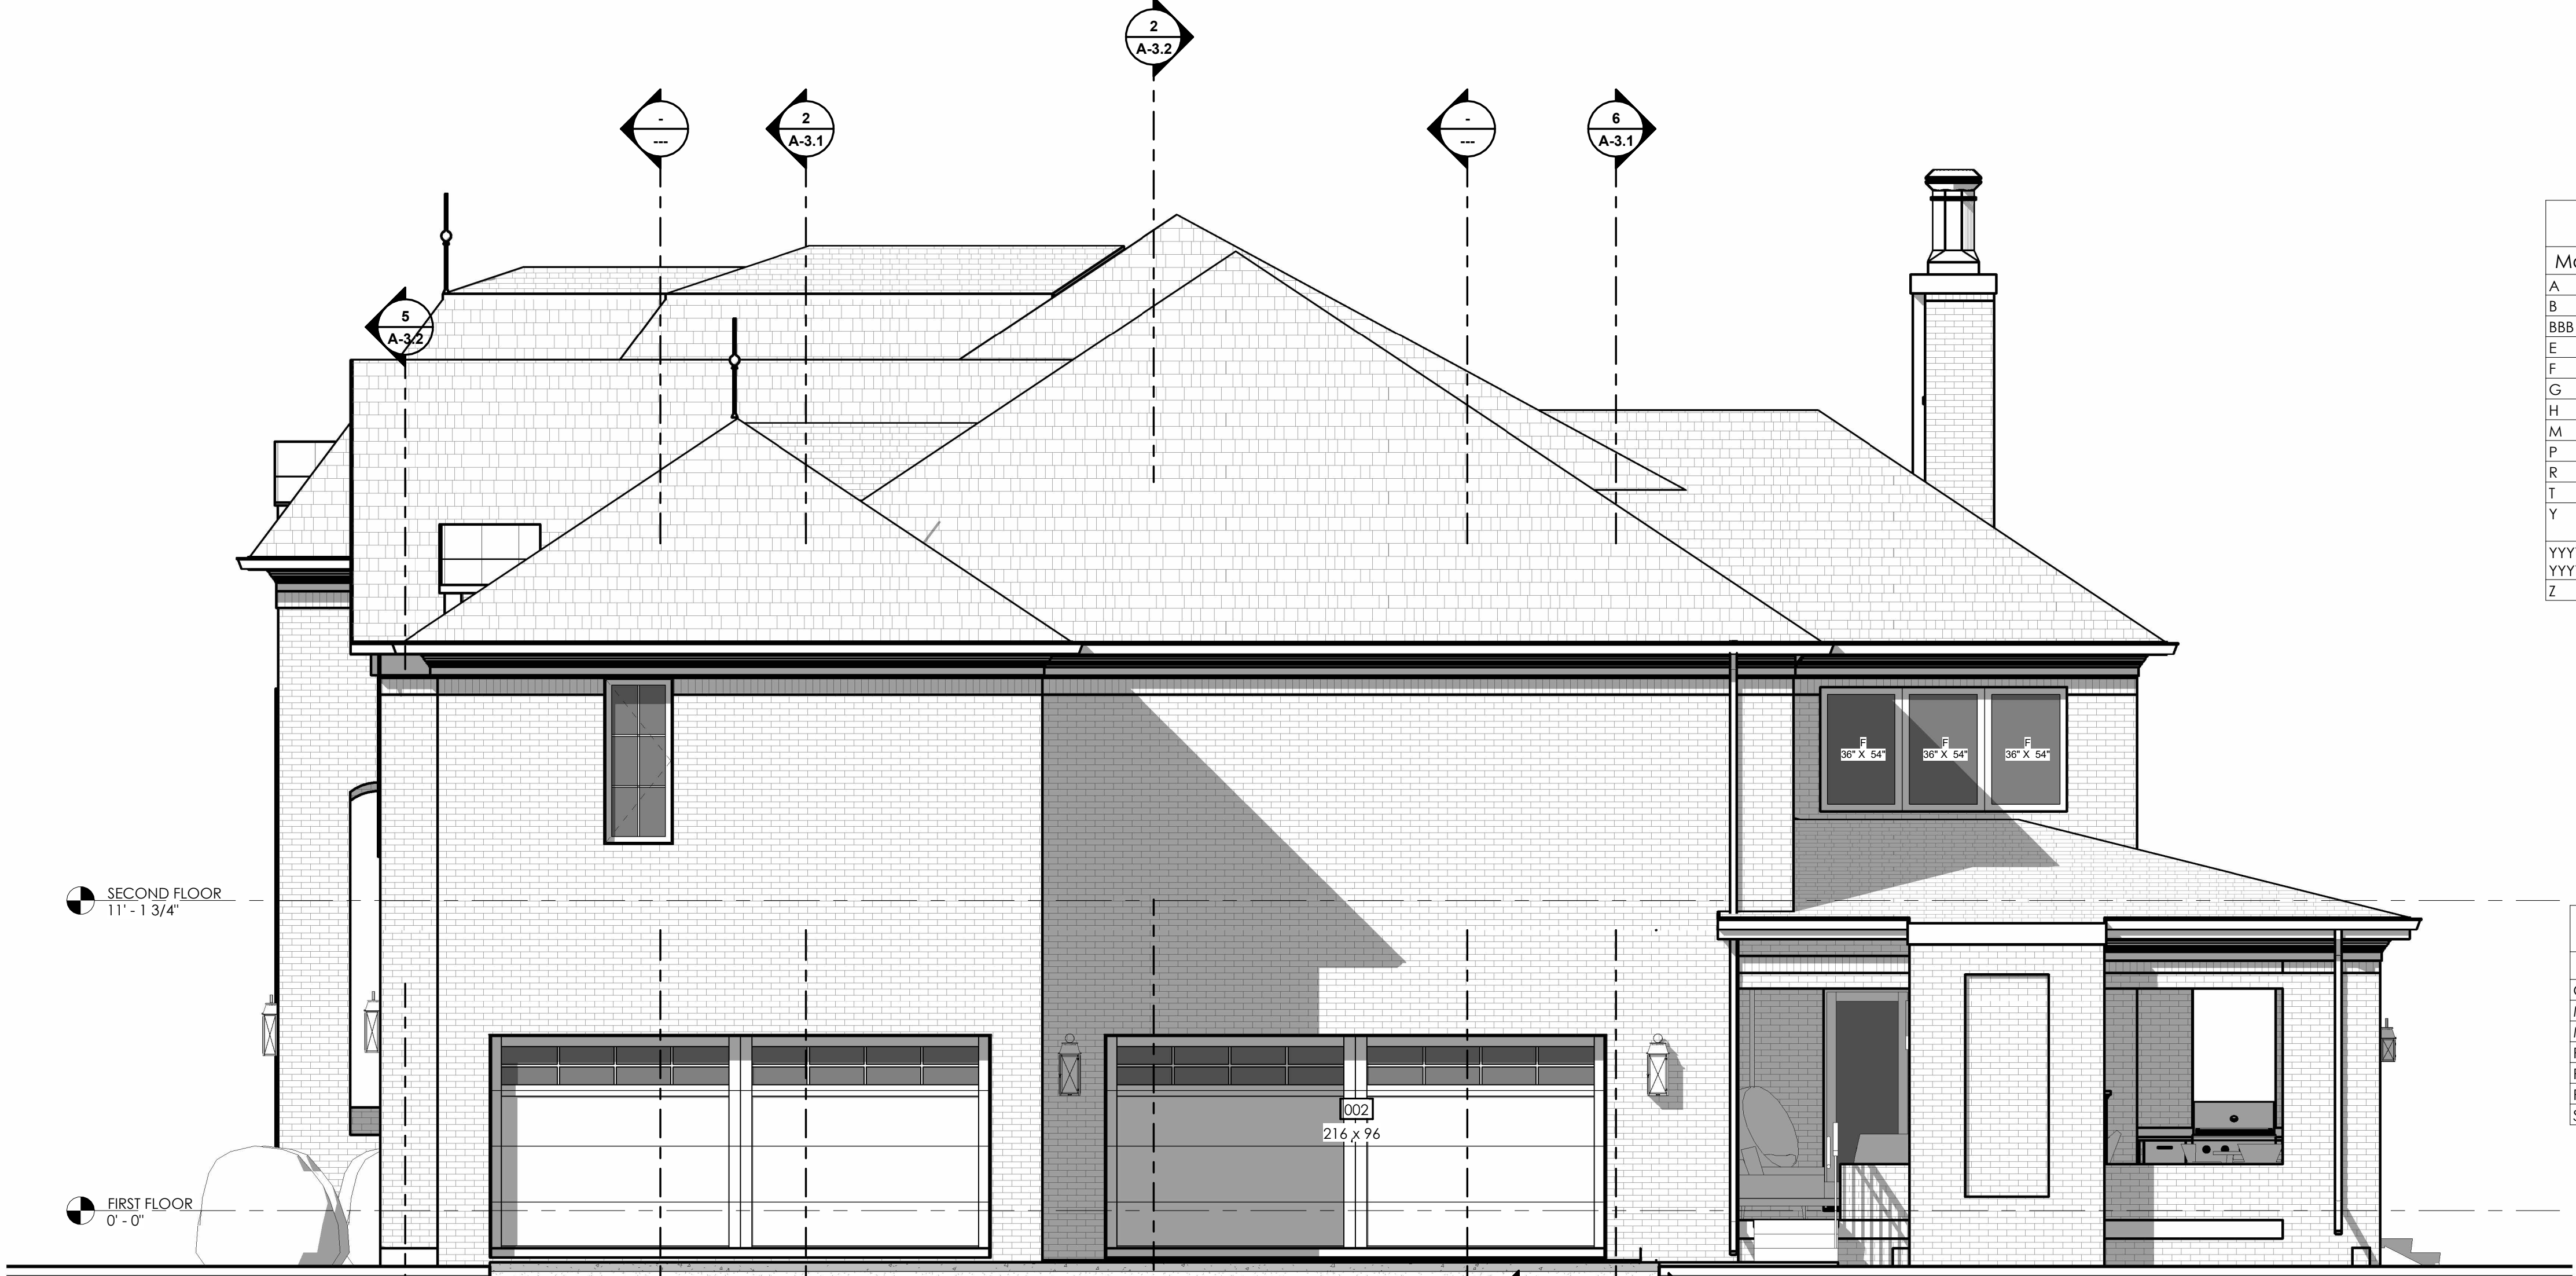

3 NORTH ELEVATION
A-2.1 SCALE: 1/4" = 1'-0"



1 EAST ELEVATION
A-2.1 SCALE: 1/4" = 1'-0"

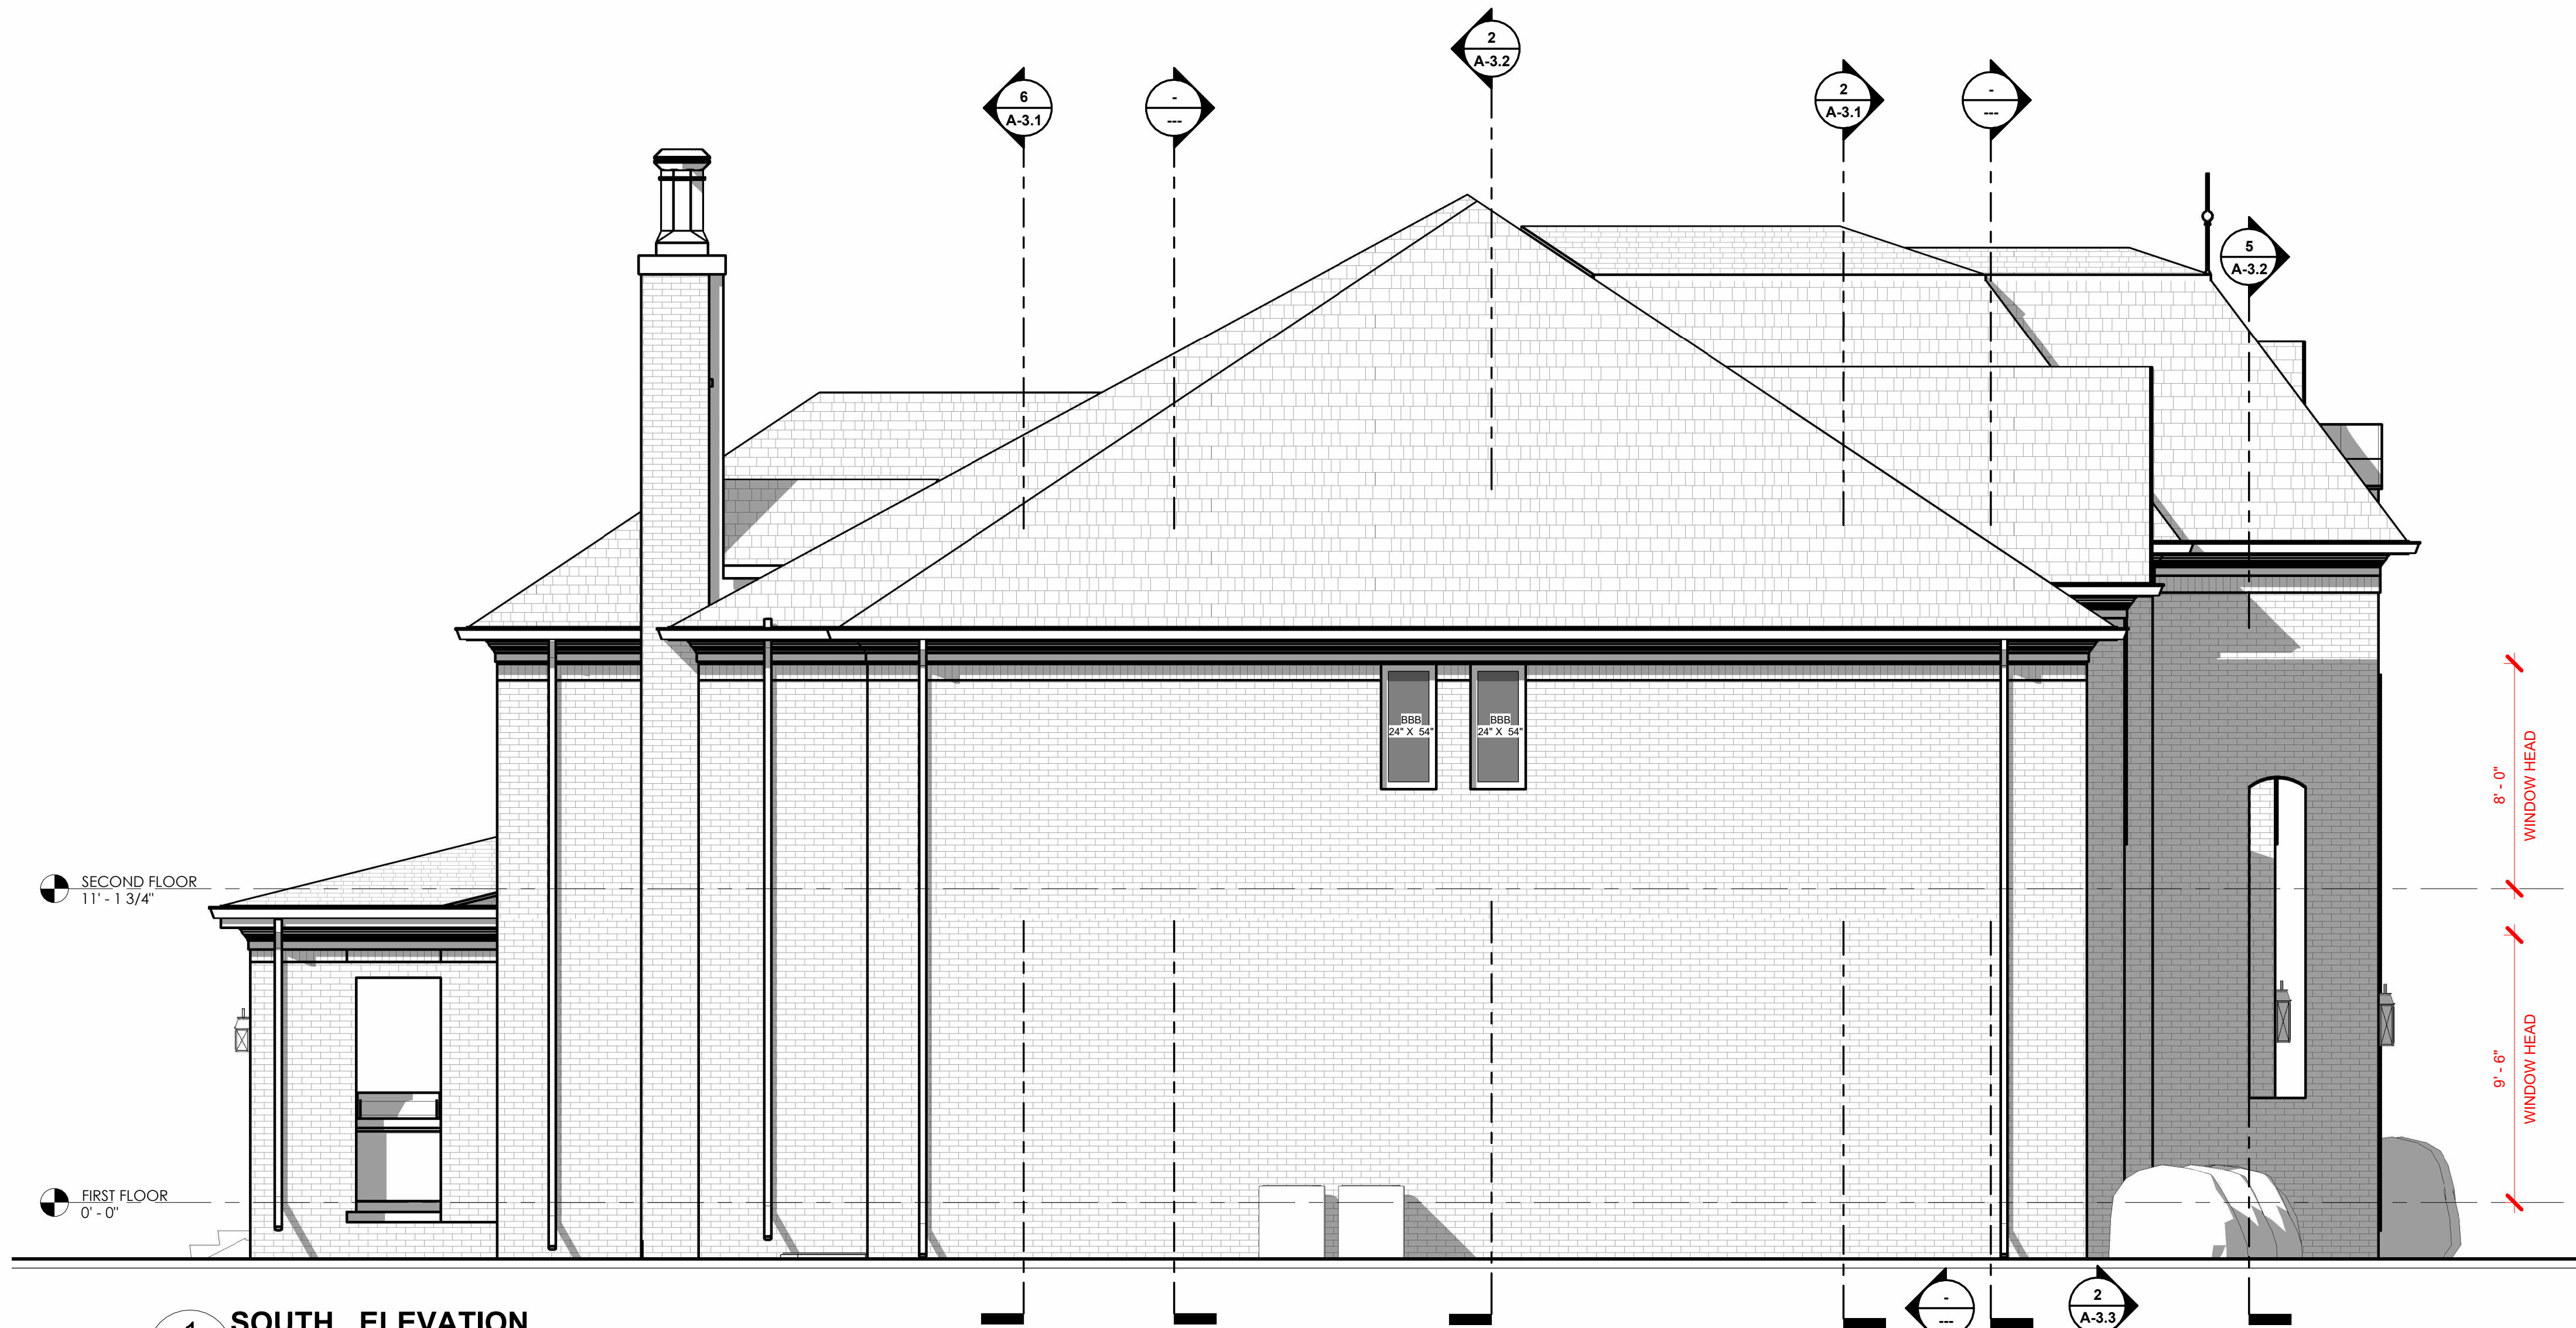

1 SOUTH ELEVATION
A-2.2 SCALE: 1/4" = 1'-0"

Window Schedule				
Mark	Type	Width	Height	Count
A	29'-1/2" x 71'-1/2"	2' - 5 1/2"	5' - 11 1/2"	10
B	29'-1/2" x 89'-1/2"	2' - 5 1/2"	7' - 5 1/2"	4
BBB	23'-1/2" x 53'-1/2"	1' - 11 1/2"	4' - 5 1/2"	3
E	47'-1/2" x 95'-1/2"	3' - 11 1/2"	7' - 11 1/2"	10
F	35'-1/2" x 53'-1/2"	2' - 11 1/2"	4' - 5 1/2"	3
G	29'-1/2" x 89'-1/2" NO DL	2' - 5 1/2"	7' - 5 1/2"	3
H	29'-1/2" x 71'-1/2" No DL	2' - 5 1/2"	5' - 11 1/2"	3
M	24" Diameter	2' - 0"		2
P	29'-1/2" x 53'-1/2"	2' - 5 1/2"	4' - 5 1/2"	1
R	Custom2 2	4' - 11 3/4"	4' - 1"	3
T	Custom4	5' - 11 3/4"	6' - 1"	1
Y	Basement_Egress_Window_Well_134' - 0"	4' - 0"	4' - 0"	1
YYYYY	35'-1/2" x 59'-1/2"	2' - 11 1/2"	4' - 11 1/2"	4
Z	29'-1/2" x 95'-1/2"	2' - 5 1/2"	7' - 11 1/2"	2

50



2 WEST ELEVATION
A-2.2 SCALE: 1/4" = 1'-0"



6523 TAMMARA CK DR.
TROY, MI 48098
248-854-0545
DALLEWDESIGN@GMAIL.COM
WWW.DALLEWDESIGN.ILLIC.COM

REVISIONS

NO.	DATE	DESCRIPTION
1	06/05/26	DESIGN 2
2	06/18/26	PRELIM. PRICE

PROJECT NAME

PATEL RESIDENCE
13515 APPLE CREST CT.
PLYMOUTH TOWNSHIP, MI
48170

SHEET TITLE

ELEVATIONS

SHEET DATA

SCALE: 1/4" = 1'-0"
JOB:
ISSUE DATE: 07/08/26

SHEET NUMBER

A-2.2